

PORT DE LA GARE, PARIS 13^{ème}

Travaux de réparation du quai maçonné



Maître d'ouvrage

HAROPA PORT | Paris

Direction de l'Aménagement

1 quai de Grenelle – 75015 Paris

Tél : 06.69.51.38.83



Maître d'œuvre

HAROPA PORT | Paris

Direction de l'Équipement et de l'Ingénierie

1 quai de Grenelle – 75015 Paris

Tél : 06.32.96.05.41



Coordonnateur SPS

COSSEC groupe DEGOUY

16 rue de la Maison Rouge - 77185 Lognes

Tél : 06.82.81.44.55



AMO Environnement

ESSOR Ingénierie

10 rue de Rome - 75008 Paris

Tél : 06.72.13.95.16



Entreprise

Océlian


12 - 14 rue Louis Blériot - 92500 RUEIL MALMAISON

Tél : 01 57 98 83 77



PLAN D'INSTALLATION DE CHANTIER

Date	Indice	Objet			Rédacteur	Vérificateur	Approbateur	
18/09/25	0	1 ^{ère} Diffusion			GDL	JLO	RBT	
Affaire	Phase	Émetteur	Domaine	Type doc		N° document	Indice	Page
25-081	EXE	OCELIAN		PL		100	0	0

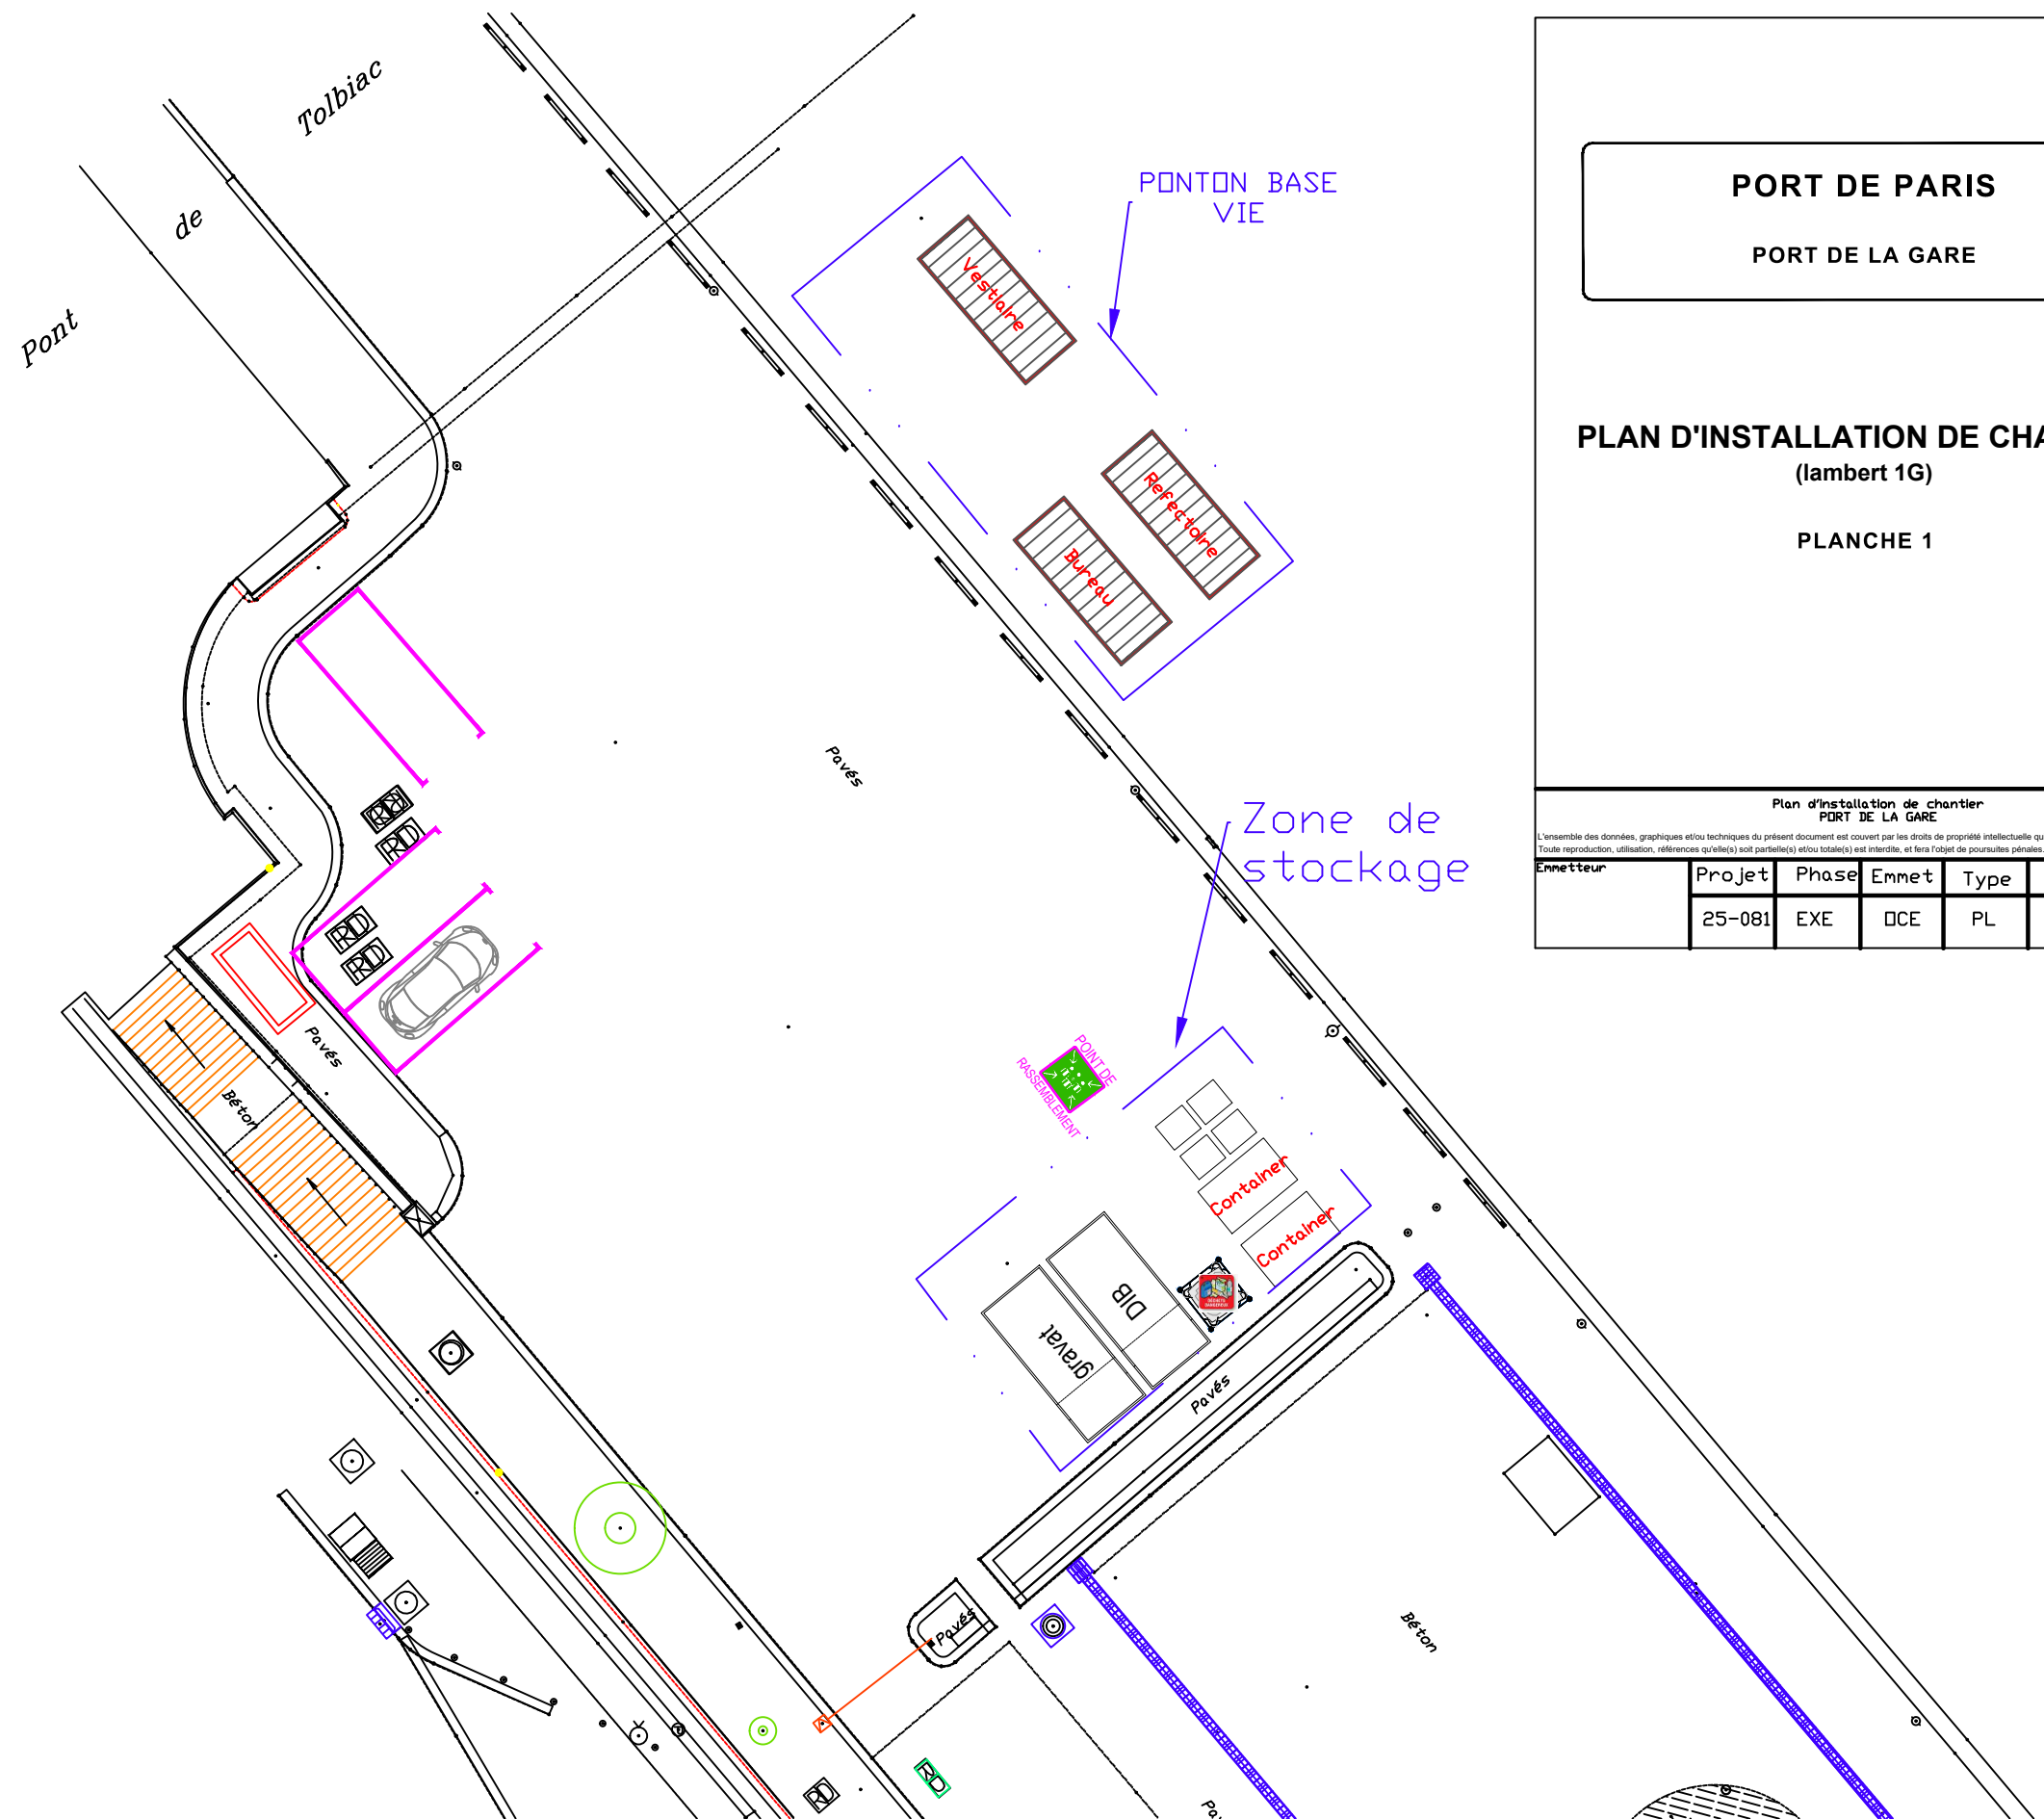

PORT DE PARIS

PORT DE LA GARE

PLAN D'INSTALLATION DE CHANTIER (lambert 1G)

PLANCHE 1

Plan d'installation de chantier PORT DE LA GARE						
L'ensemble des données, graphiques et/ou techniques du présent document est couvert par les droits de propriété intellectuelle qui bénéficient à Océlan. Toute reproduction, utilisation, référence qu'elle(s) soit partielle(s) et/ou totale(s) est interdite, et fera l'objet de poursuites pénales.						
Emetteur	Projet	Phase	Emmet	Type	N°	Index
	25-081	EXE	OCE	PL	100	0